
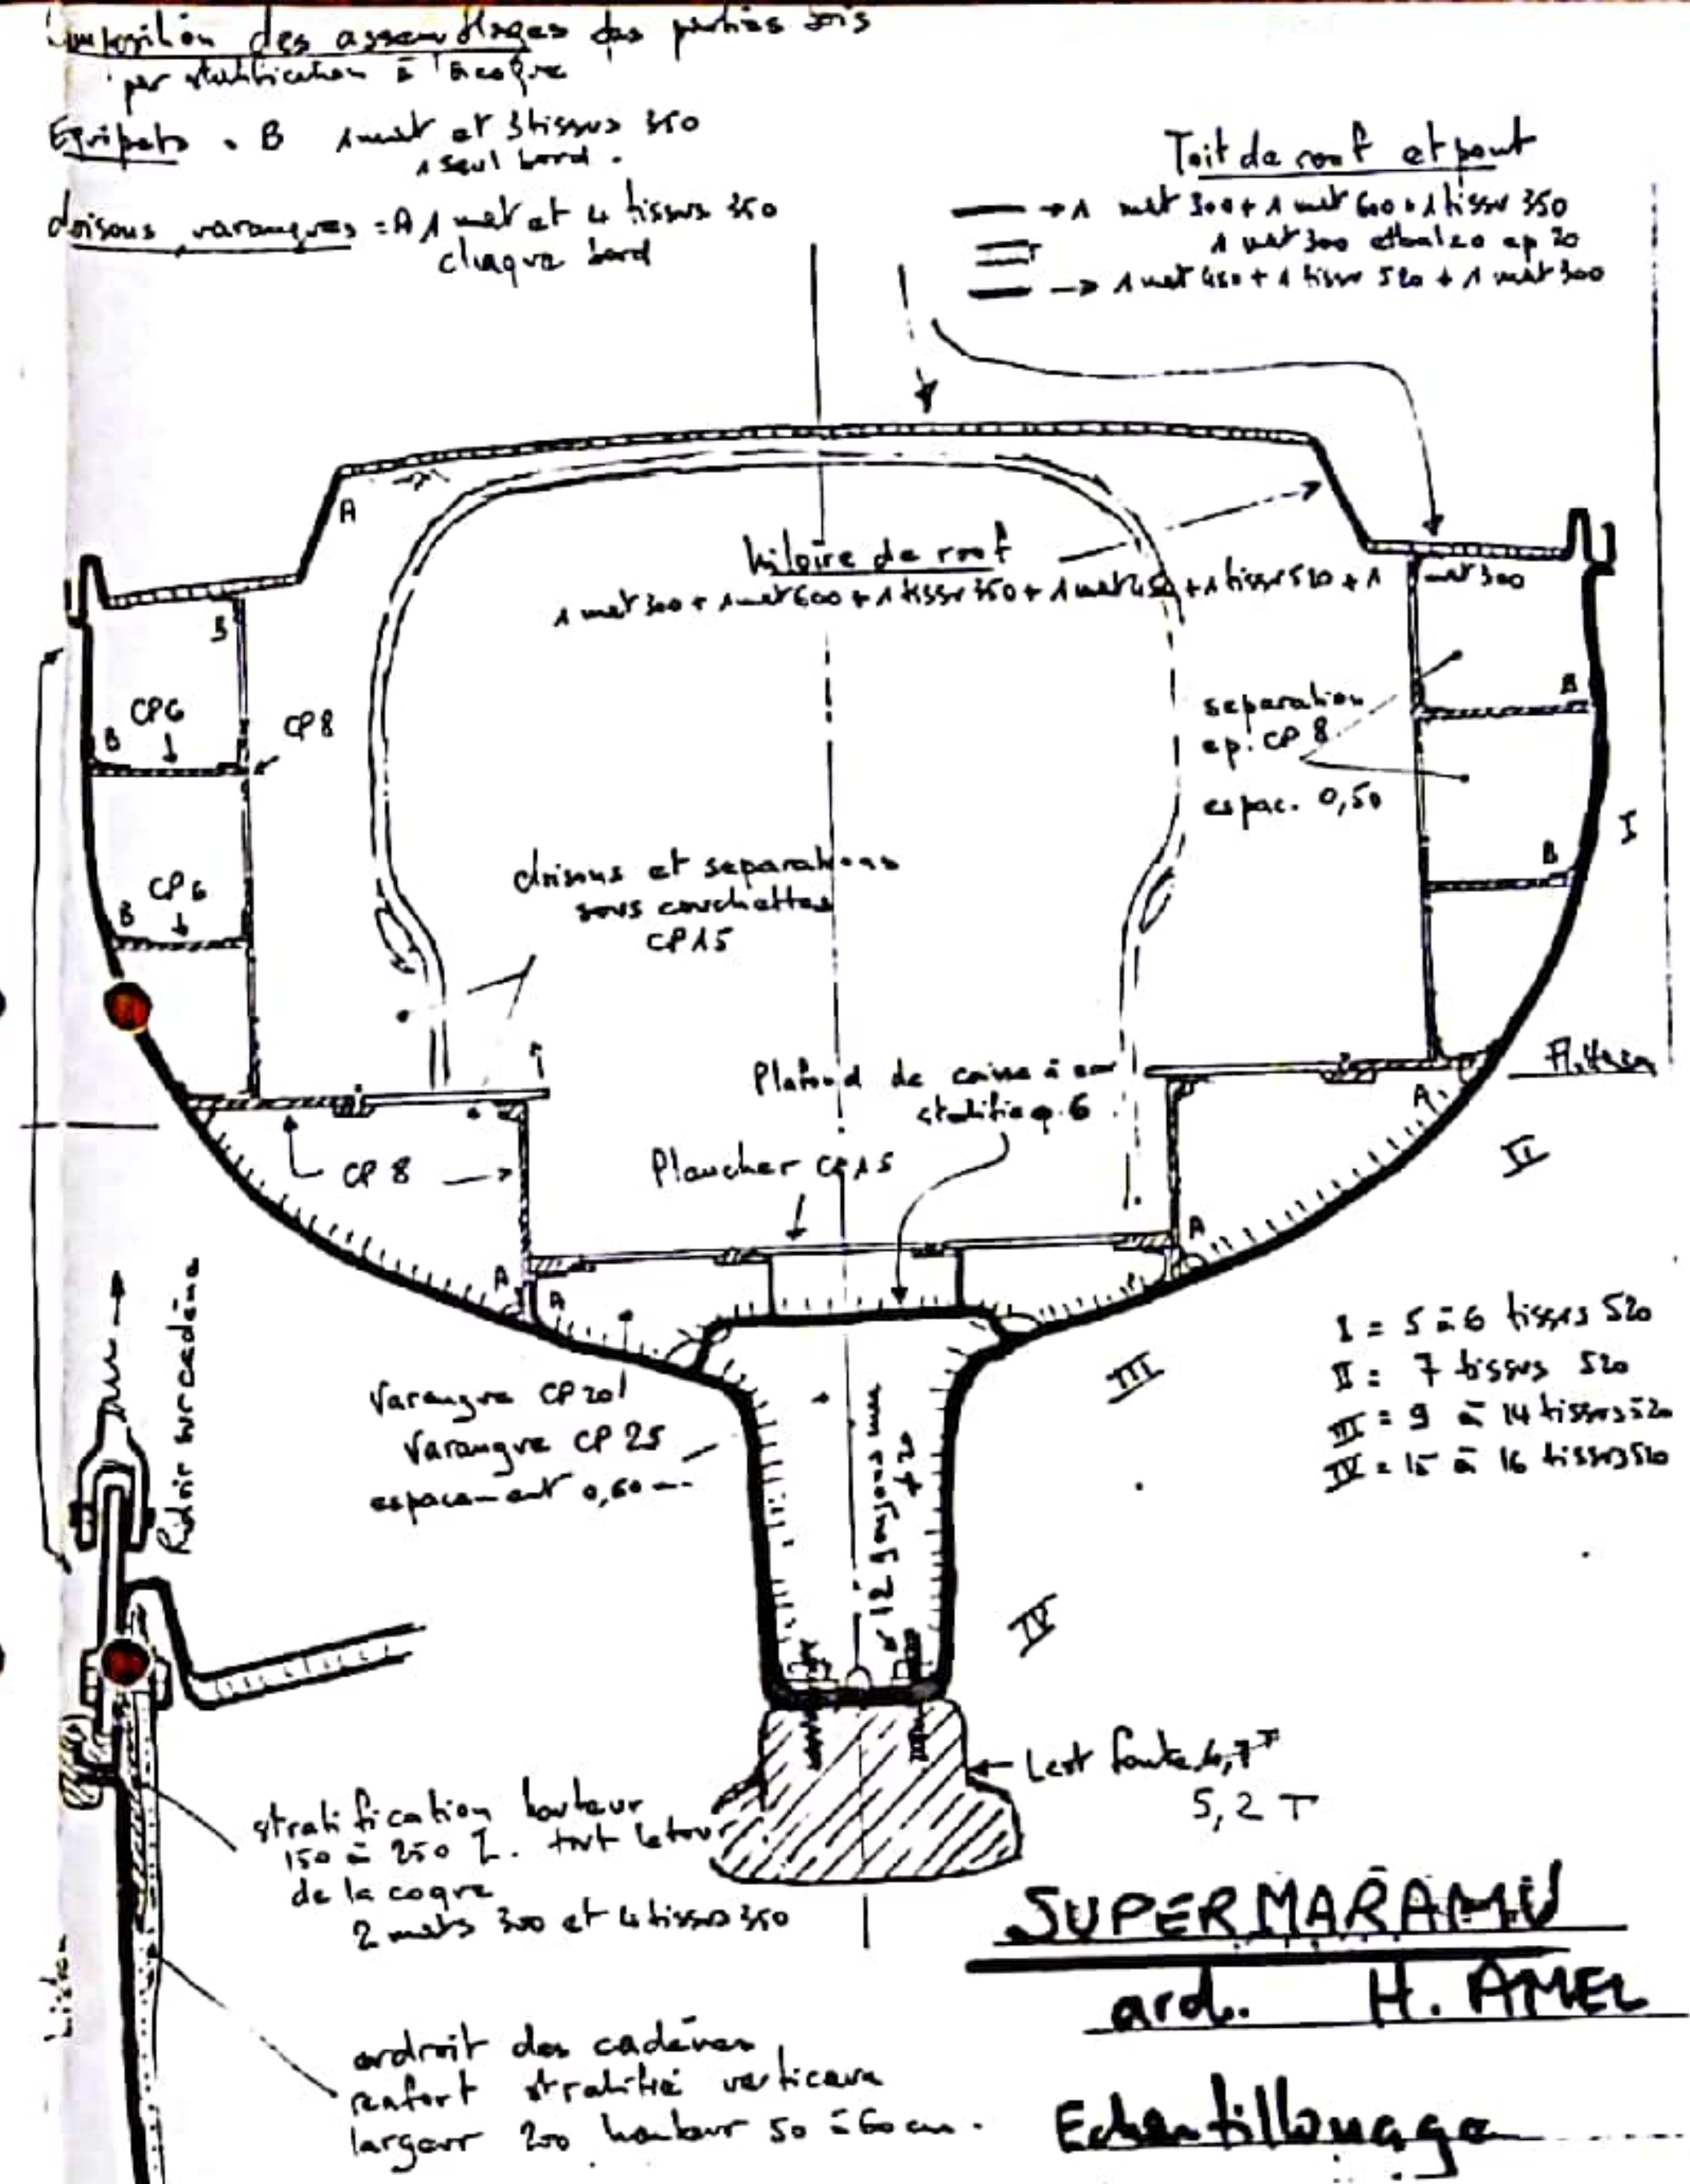


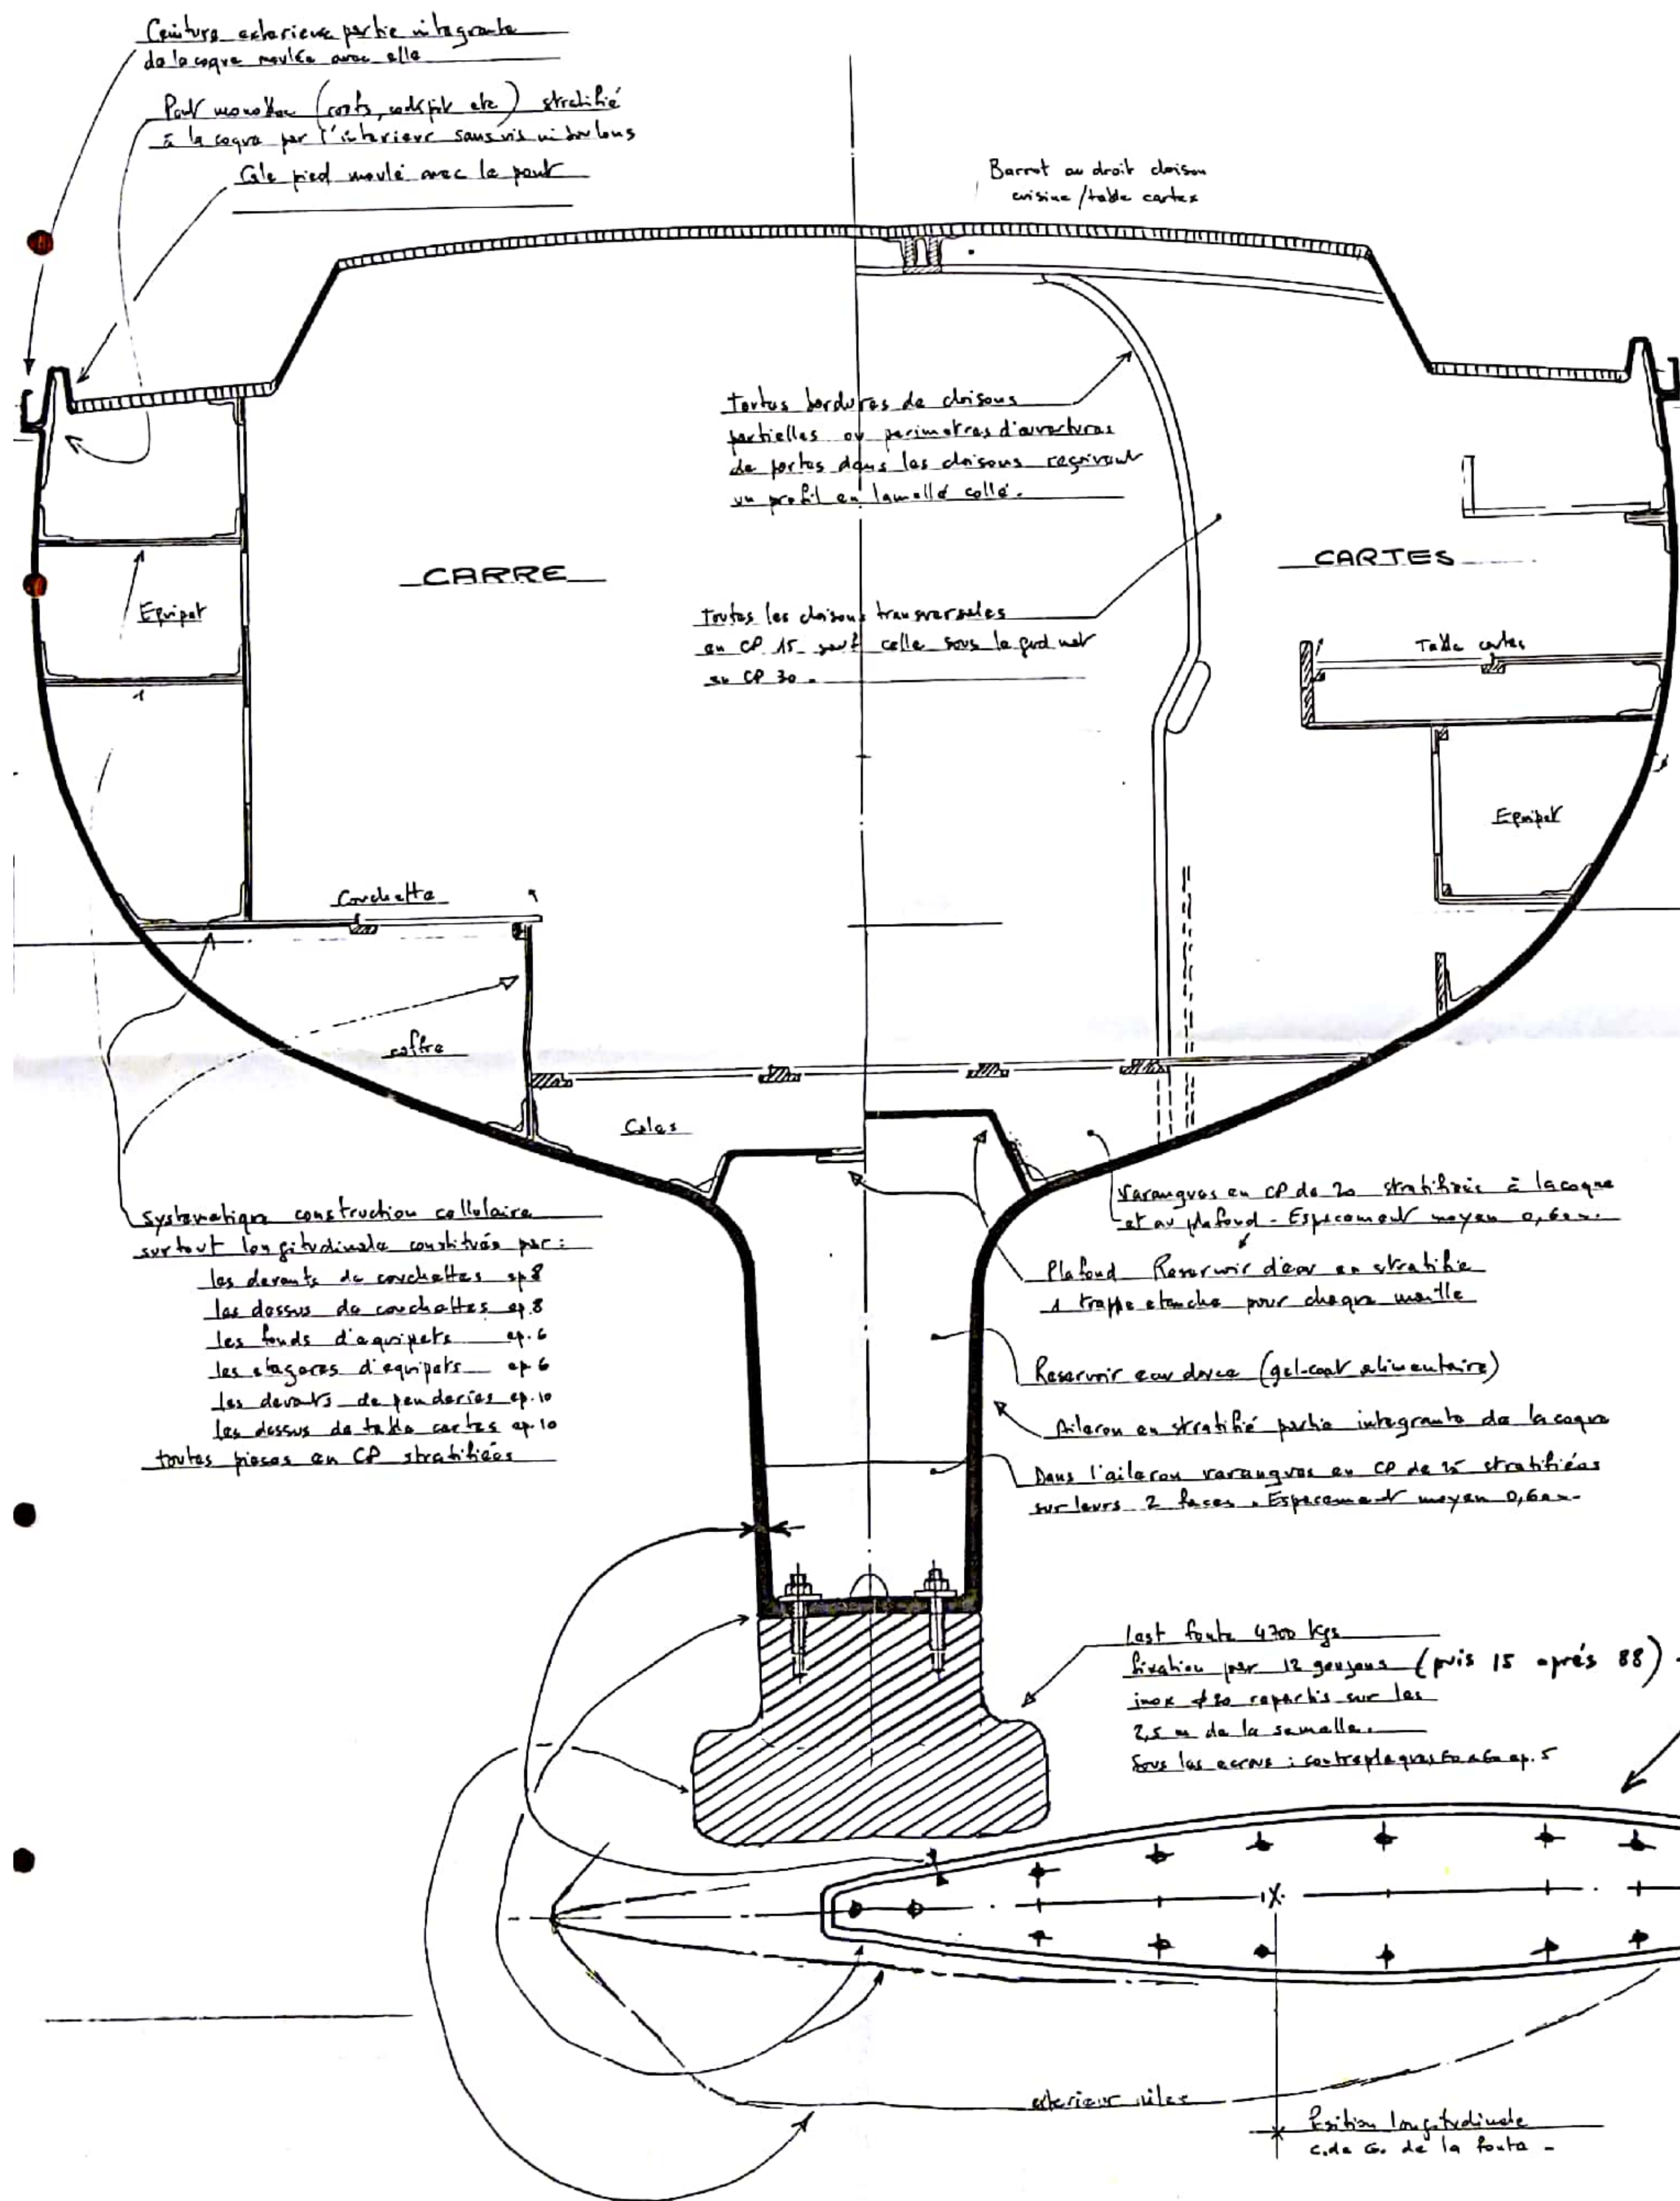

CHANTIERS AMEL

COUPE AU MÂTRE - SUPER MARAMU

Voilier de 15,8m

Architecte H. AMEL

SM 6

Edu. 1/10 - 1/20

Nov. 87