


Suspentes en inox ép. 3 utilisée
comme cadènes galv. et inter pont met

Cadènes inox ép. 3 utilisée
x les herbes pont met

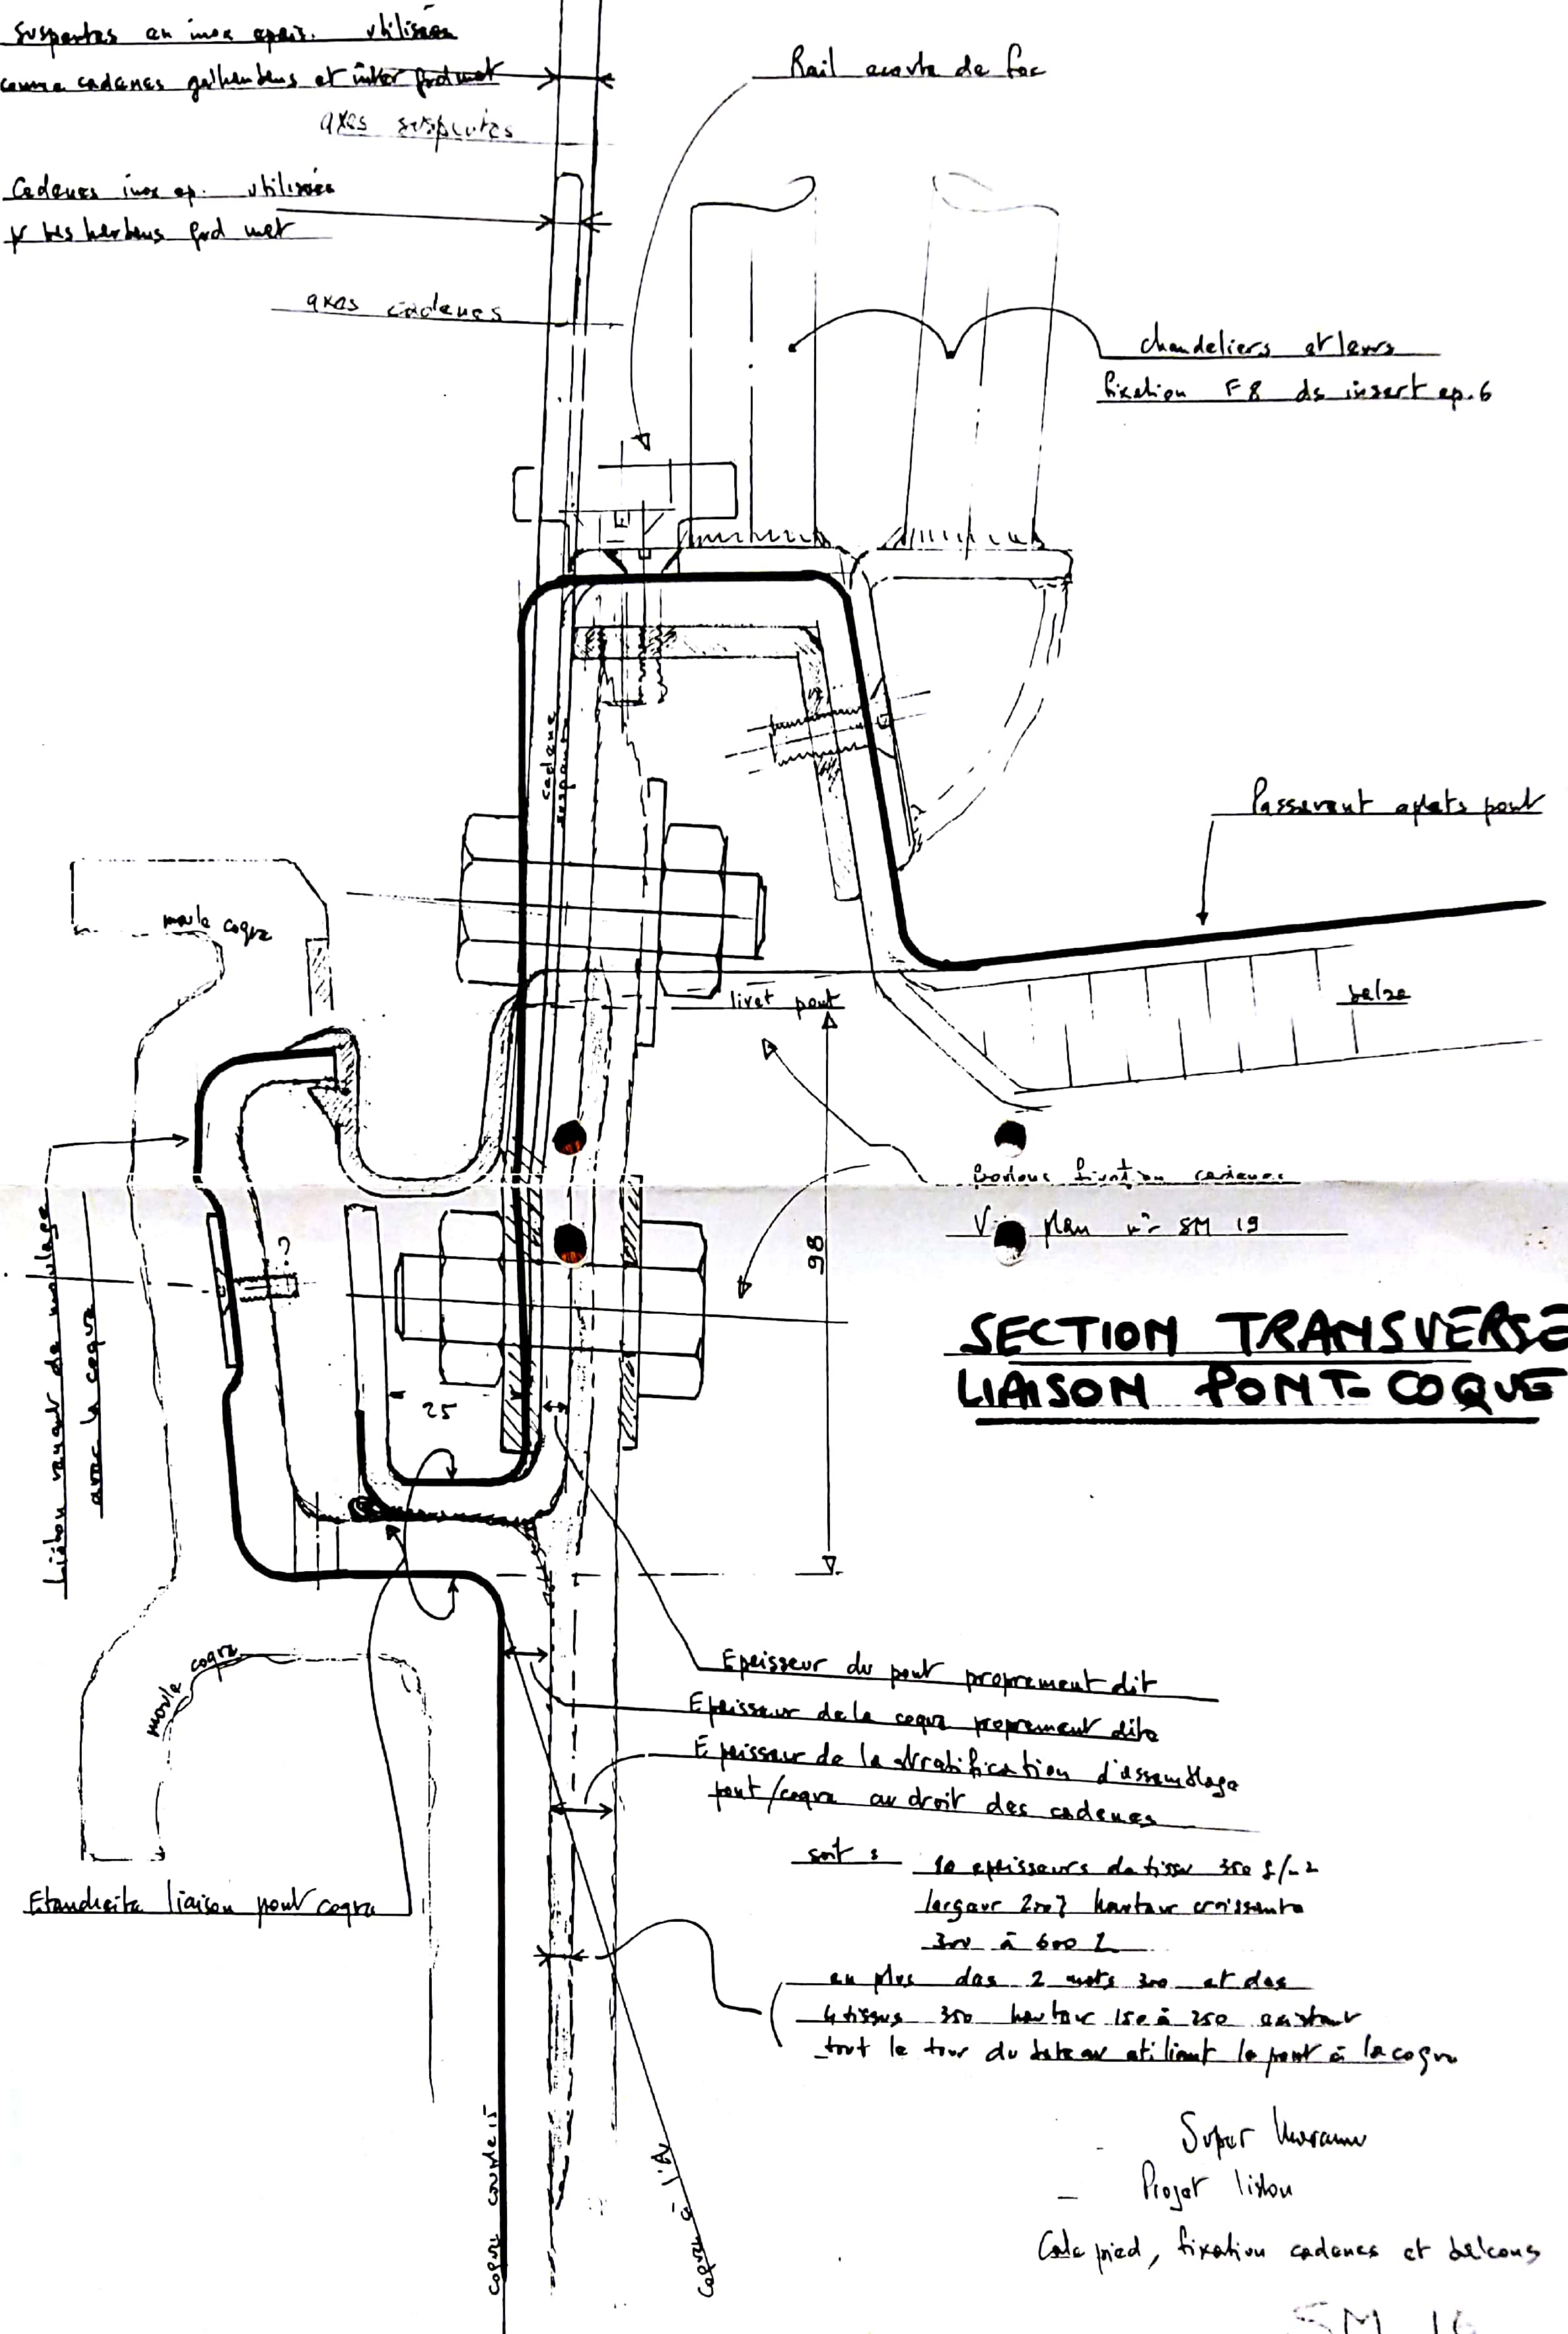

SECTION TRANSVERSE LIAISON PONT-COQUE

Epaisseur du pont proprement dit
Epaisseur de la coque proprement dite
Epaisseur de la stratification d'assemblage
pont/coque au droit des cadènes

soit : 10 épaisseurs de tissu 350 g/m²
largeur 2007 hauteur croissante
300 à 600 L

en plus des 2 nœuds 300 et des
4 tissus 350 hauteur 150 à 250 au-dessus
tout le tour du bateau reliant le pont à la coque

Super Bureau
Projet litou
Cale pied, fixation cadènes et balcons

SM 16

ach 1/ 24 Nov 87