




APPENDIX 4

Electrical drawings

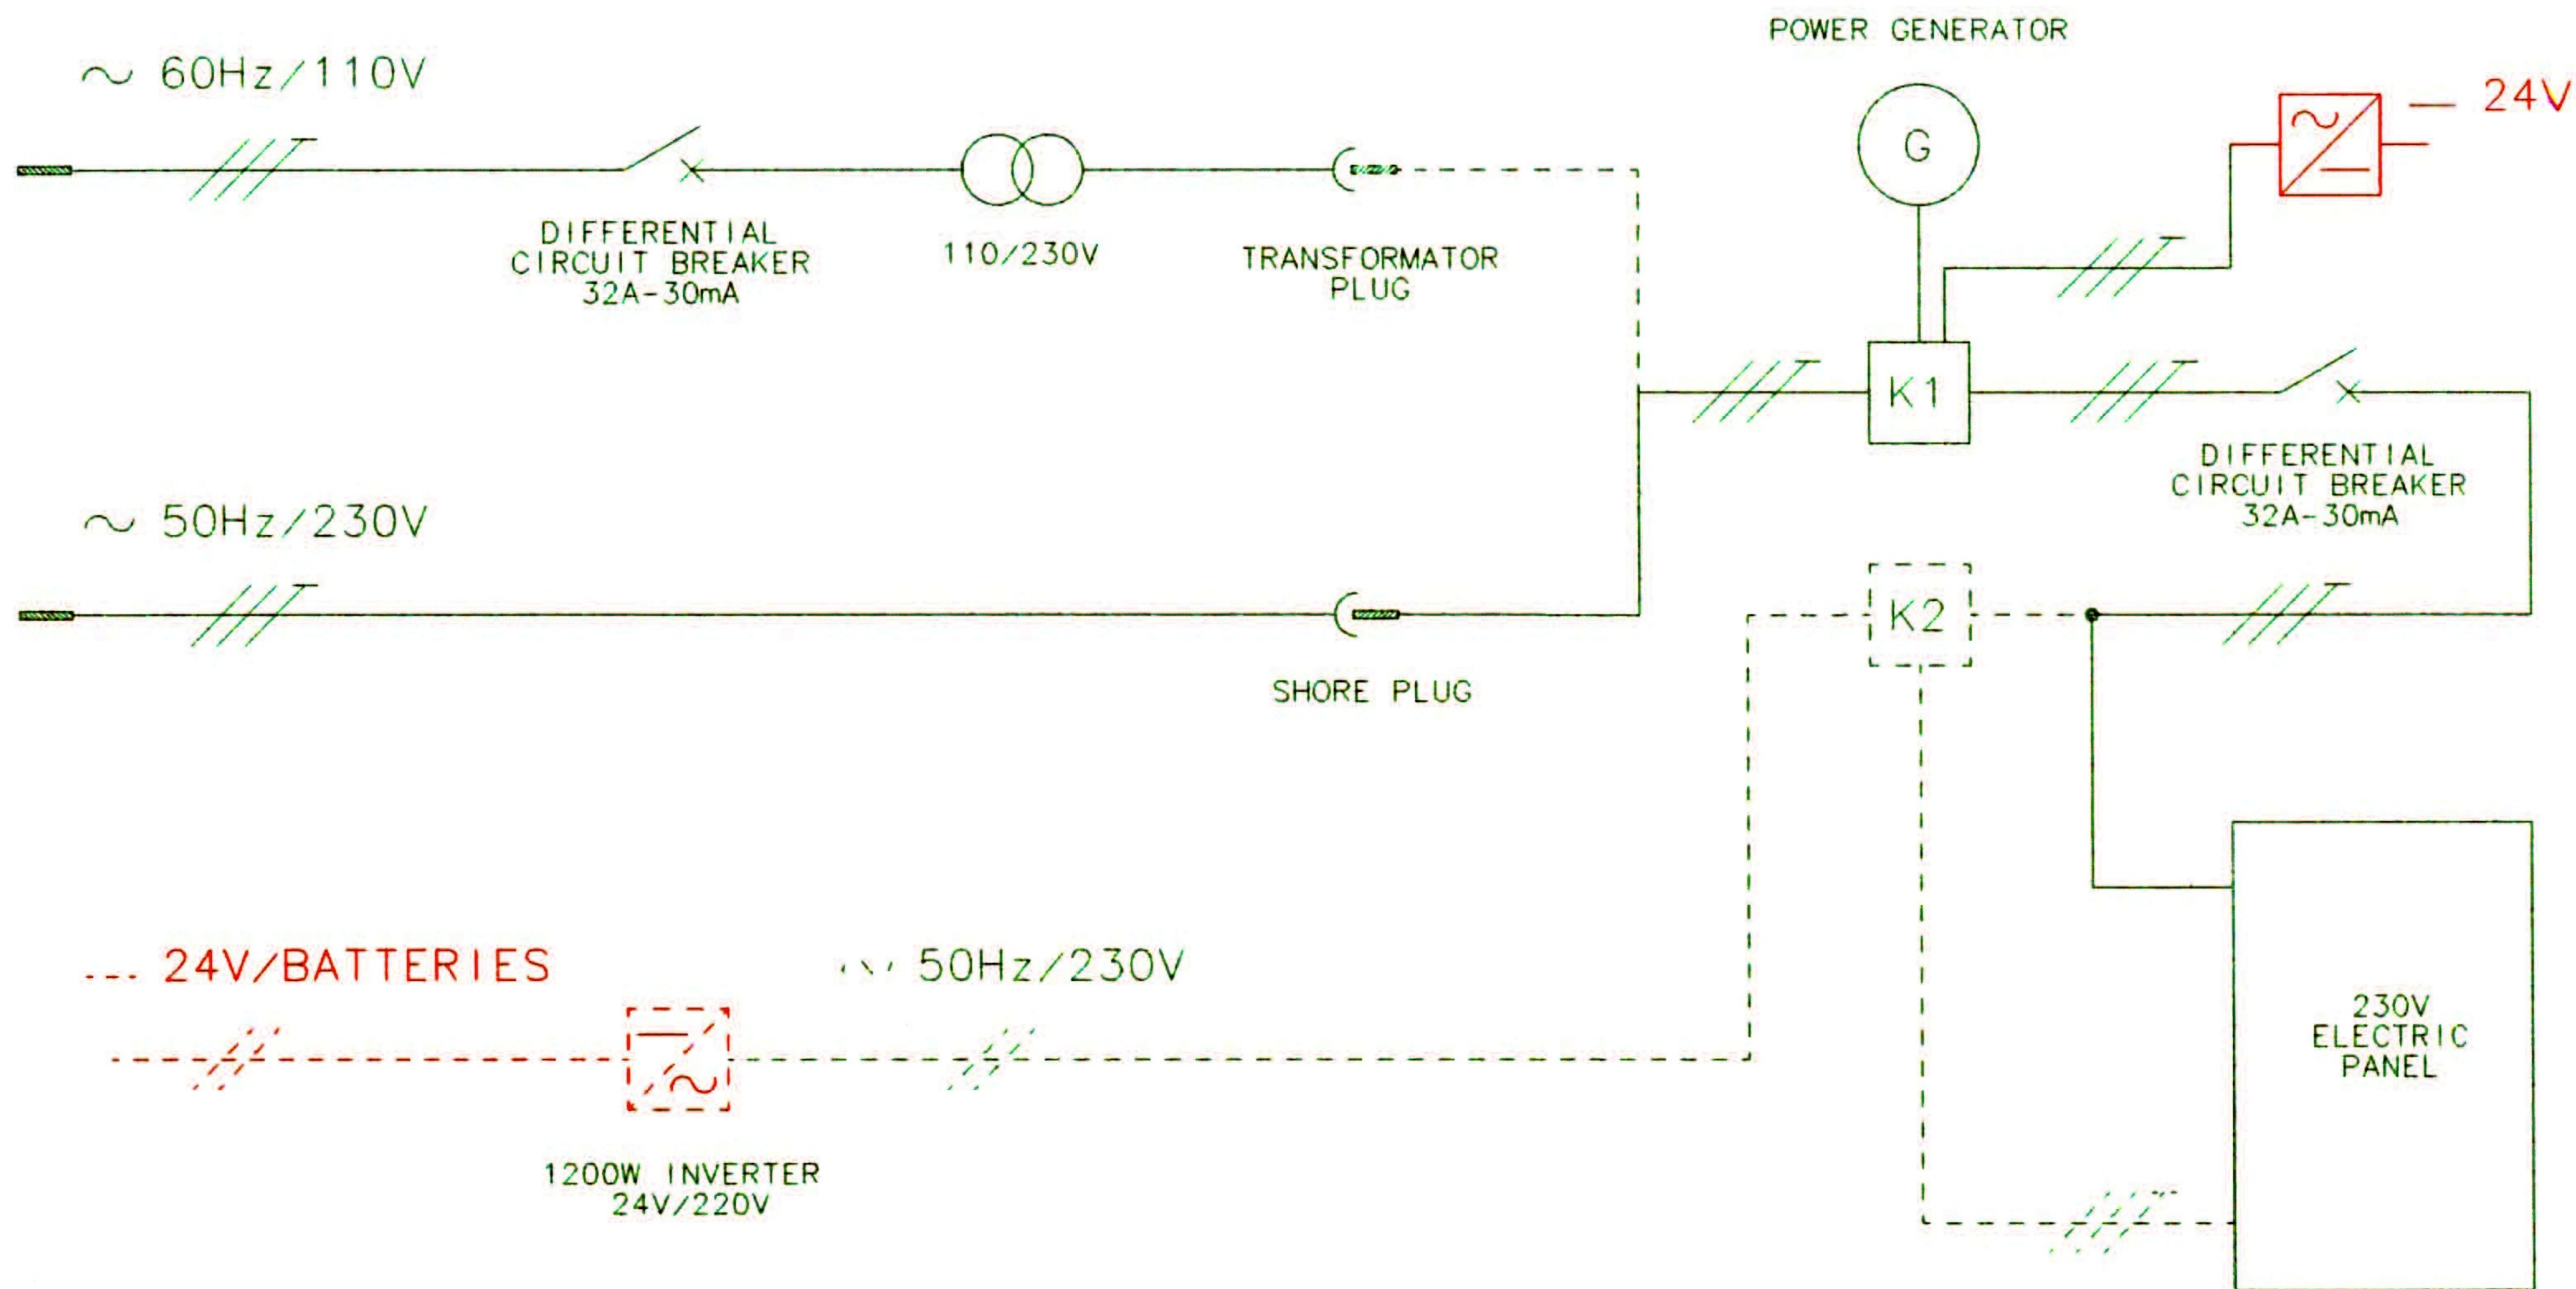

220 / 110V CIRCUIT



CHANTIERS
AMEL

Numero :

Matiere :


Ech:



Dessine par :

Dessine le :
06/12/2001

24V +

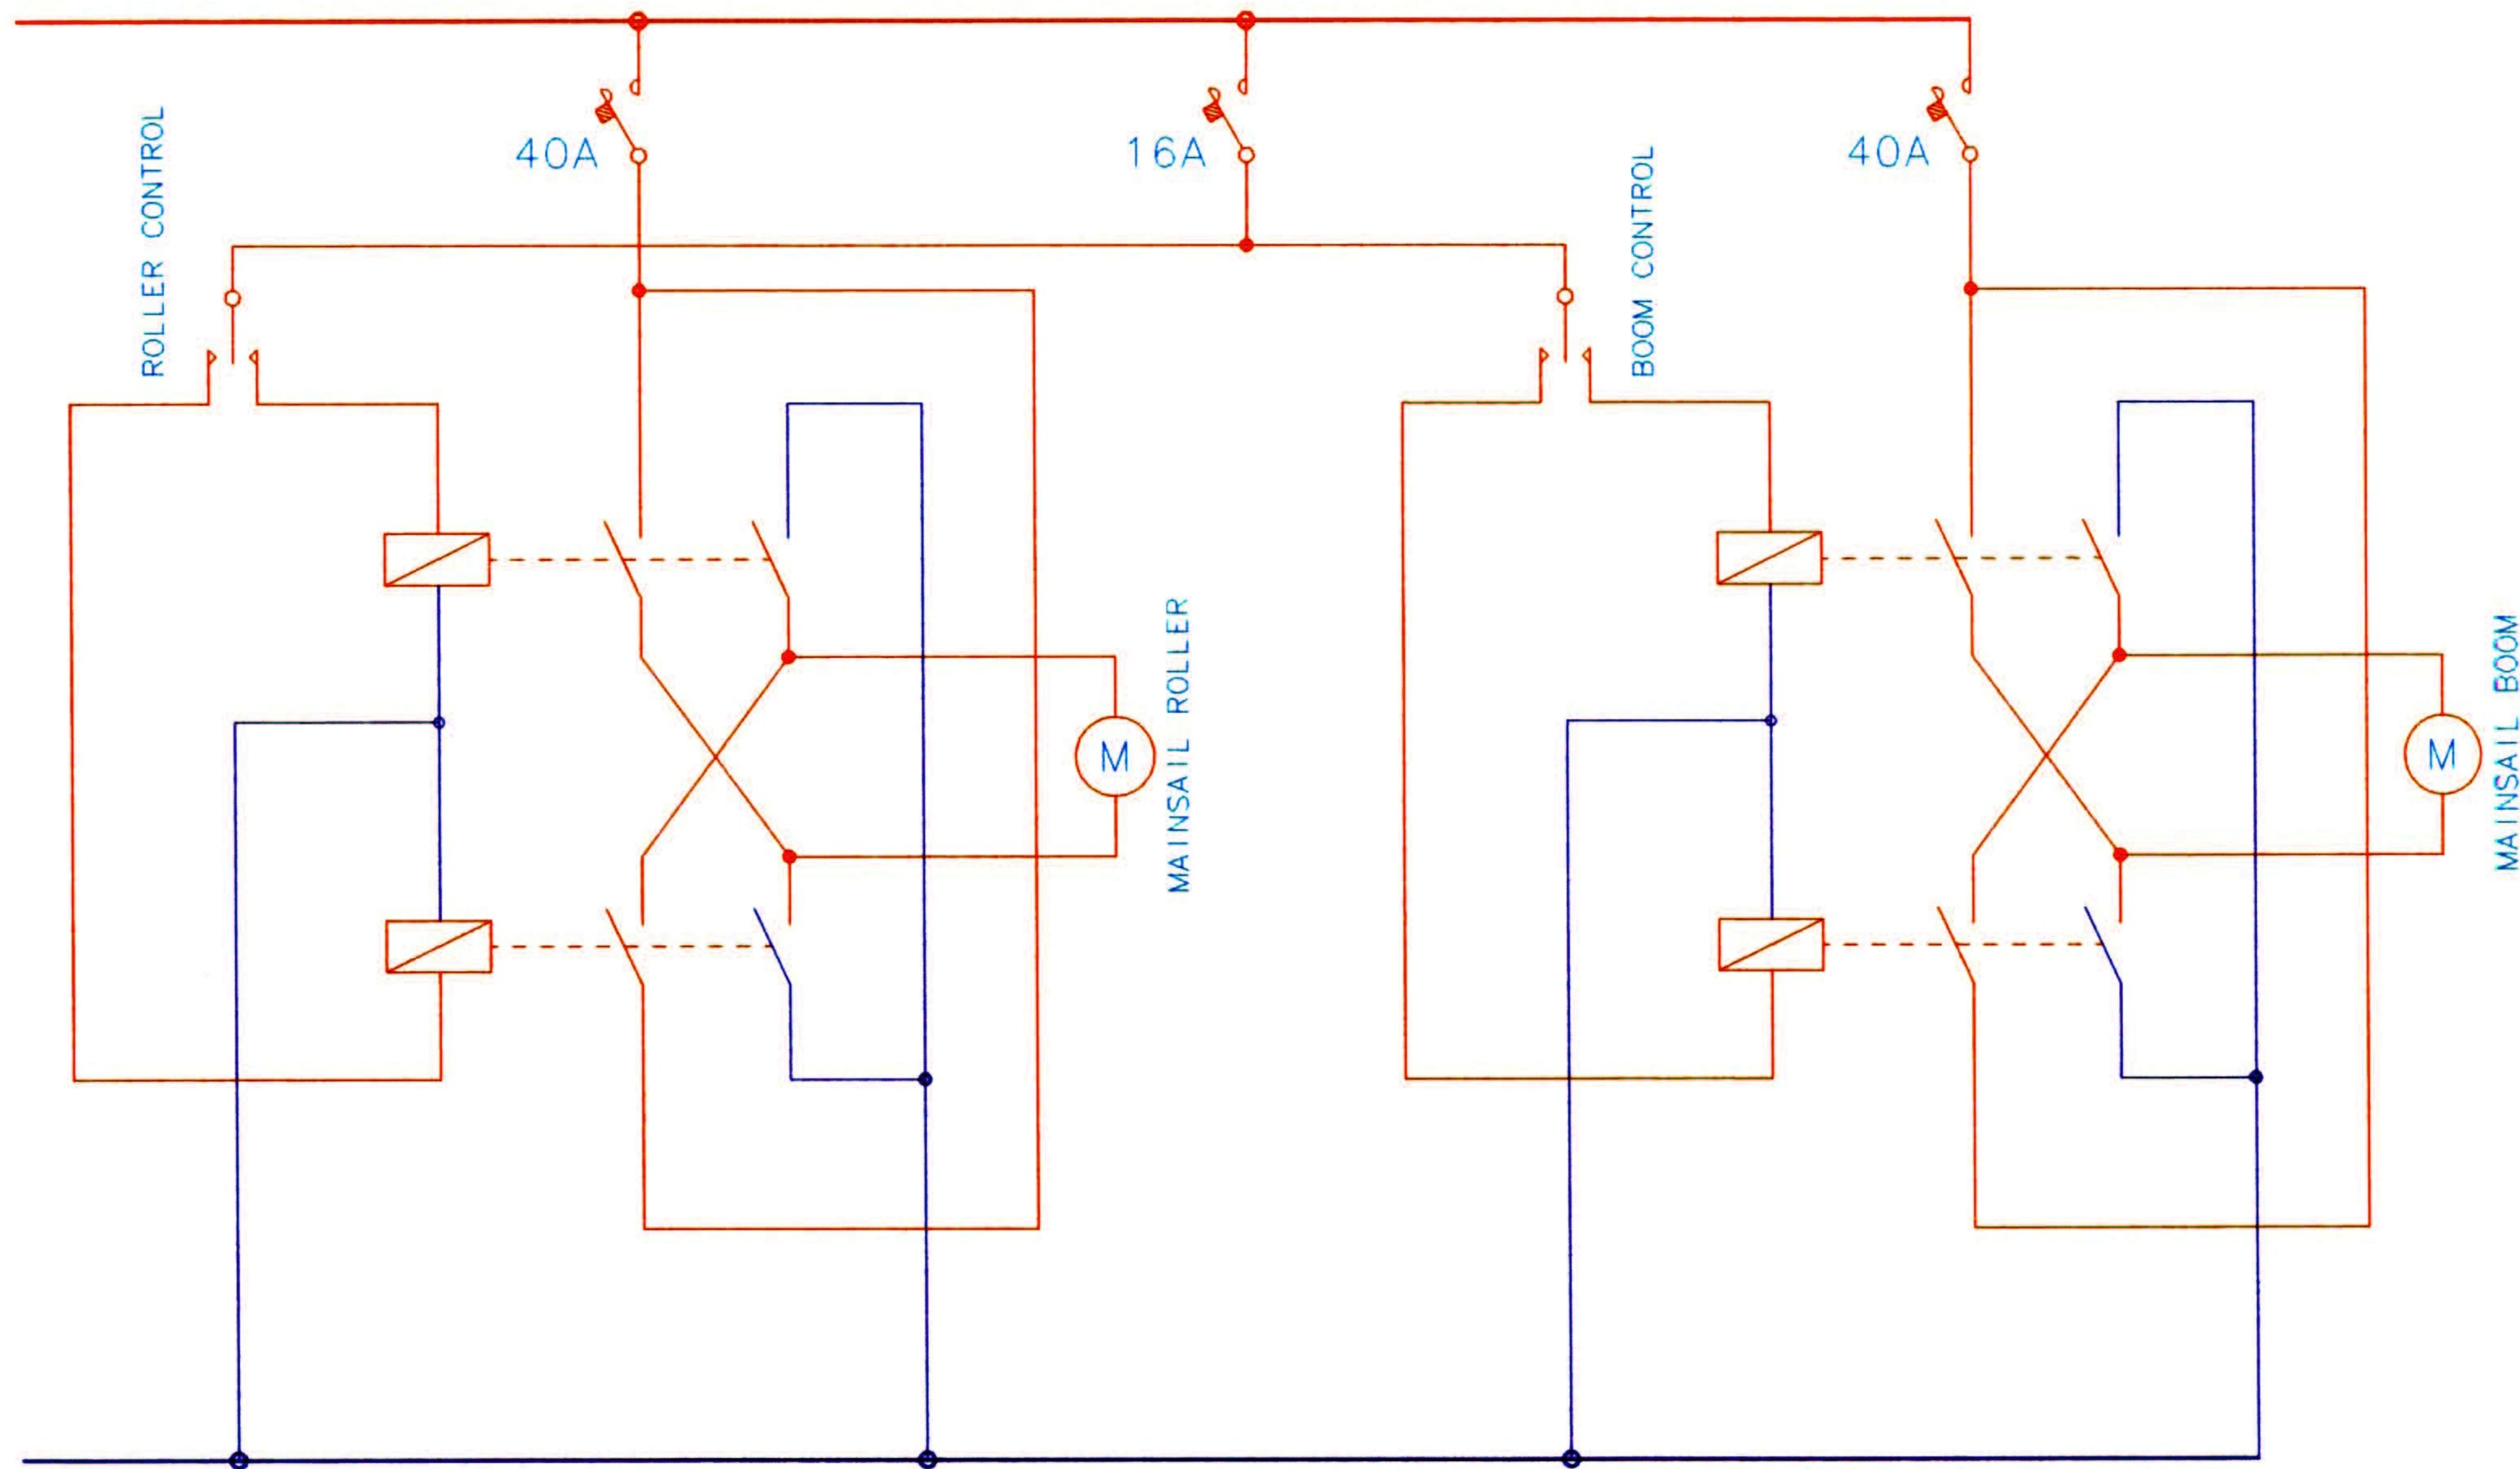

24V -

COMMAND/POWER - MAINSAIL



CHANTIERS
AMEL

Numero :

Matiere :

Ech:



Dessine par :
L. GIBOUIN

Dessine le :
06/12/2001

24V +)

16A

100A

JIB ROLLER
FURLER CONTROL

WINDLASS'
CONTROL

JIB ROLLER FURLER

WINDLASS

24V -

COMMAND/POWER - JIB/WINDLASS

Ech:




CHANTIERS
AMEL

Numero :

Dessine par :
L. GIBOUIN

Matiere :

Dessine le :
06/12/2001

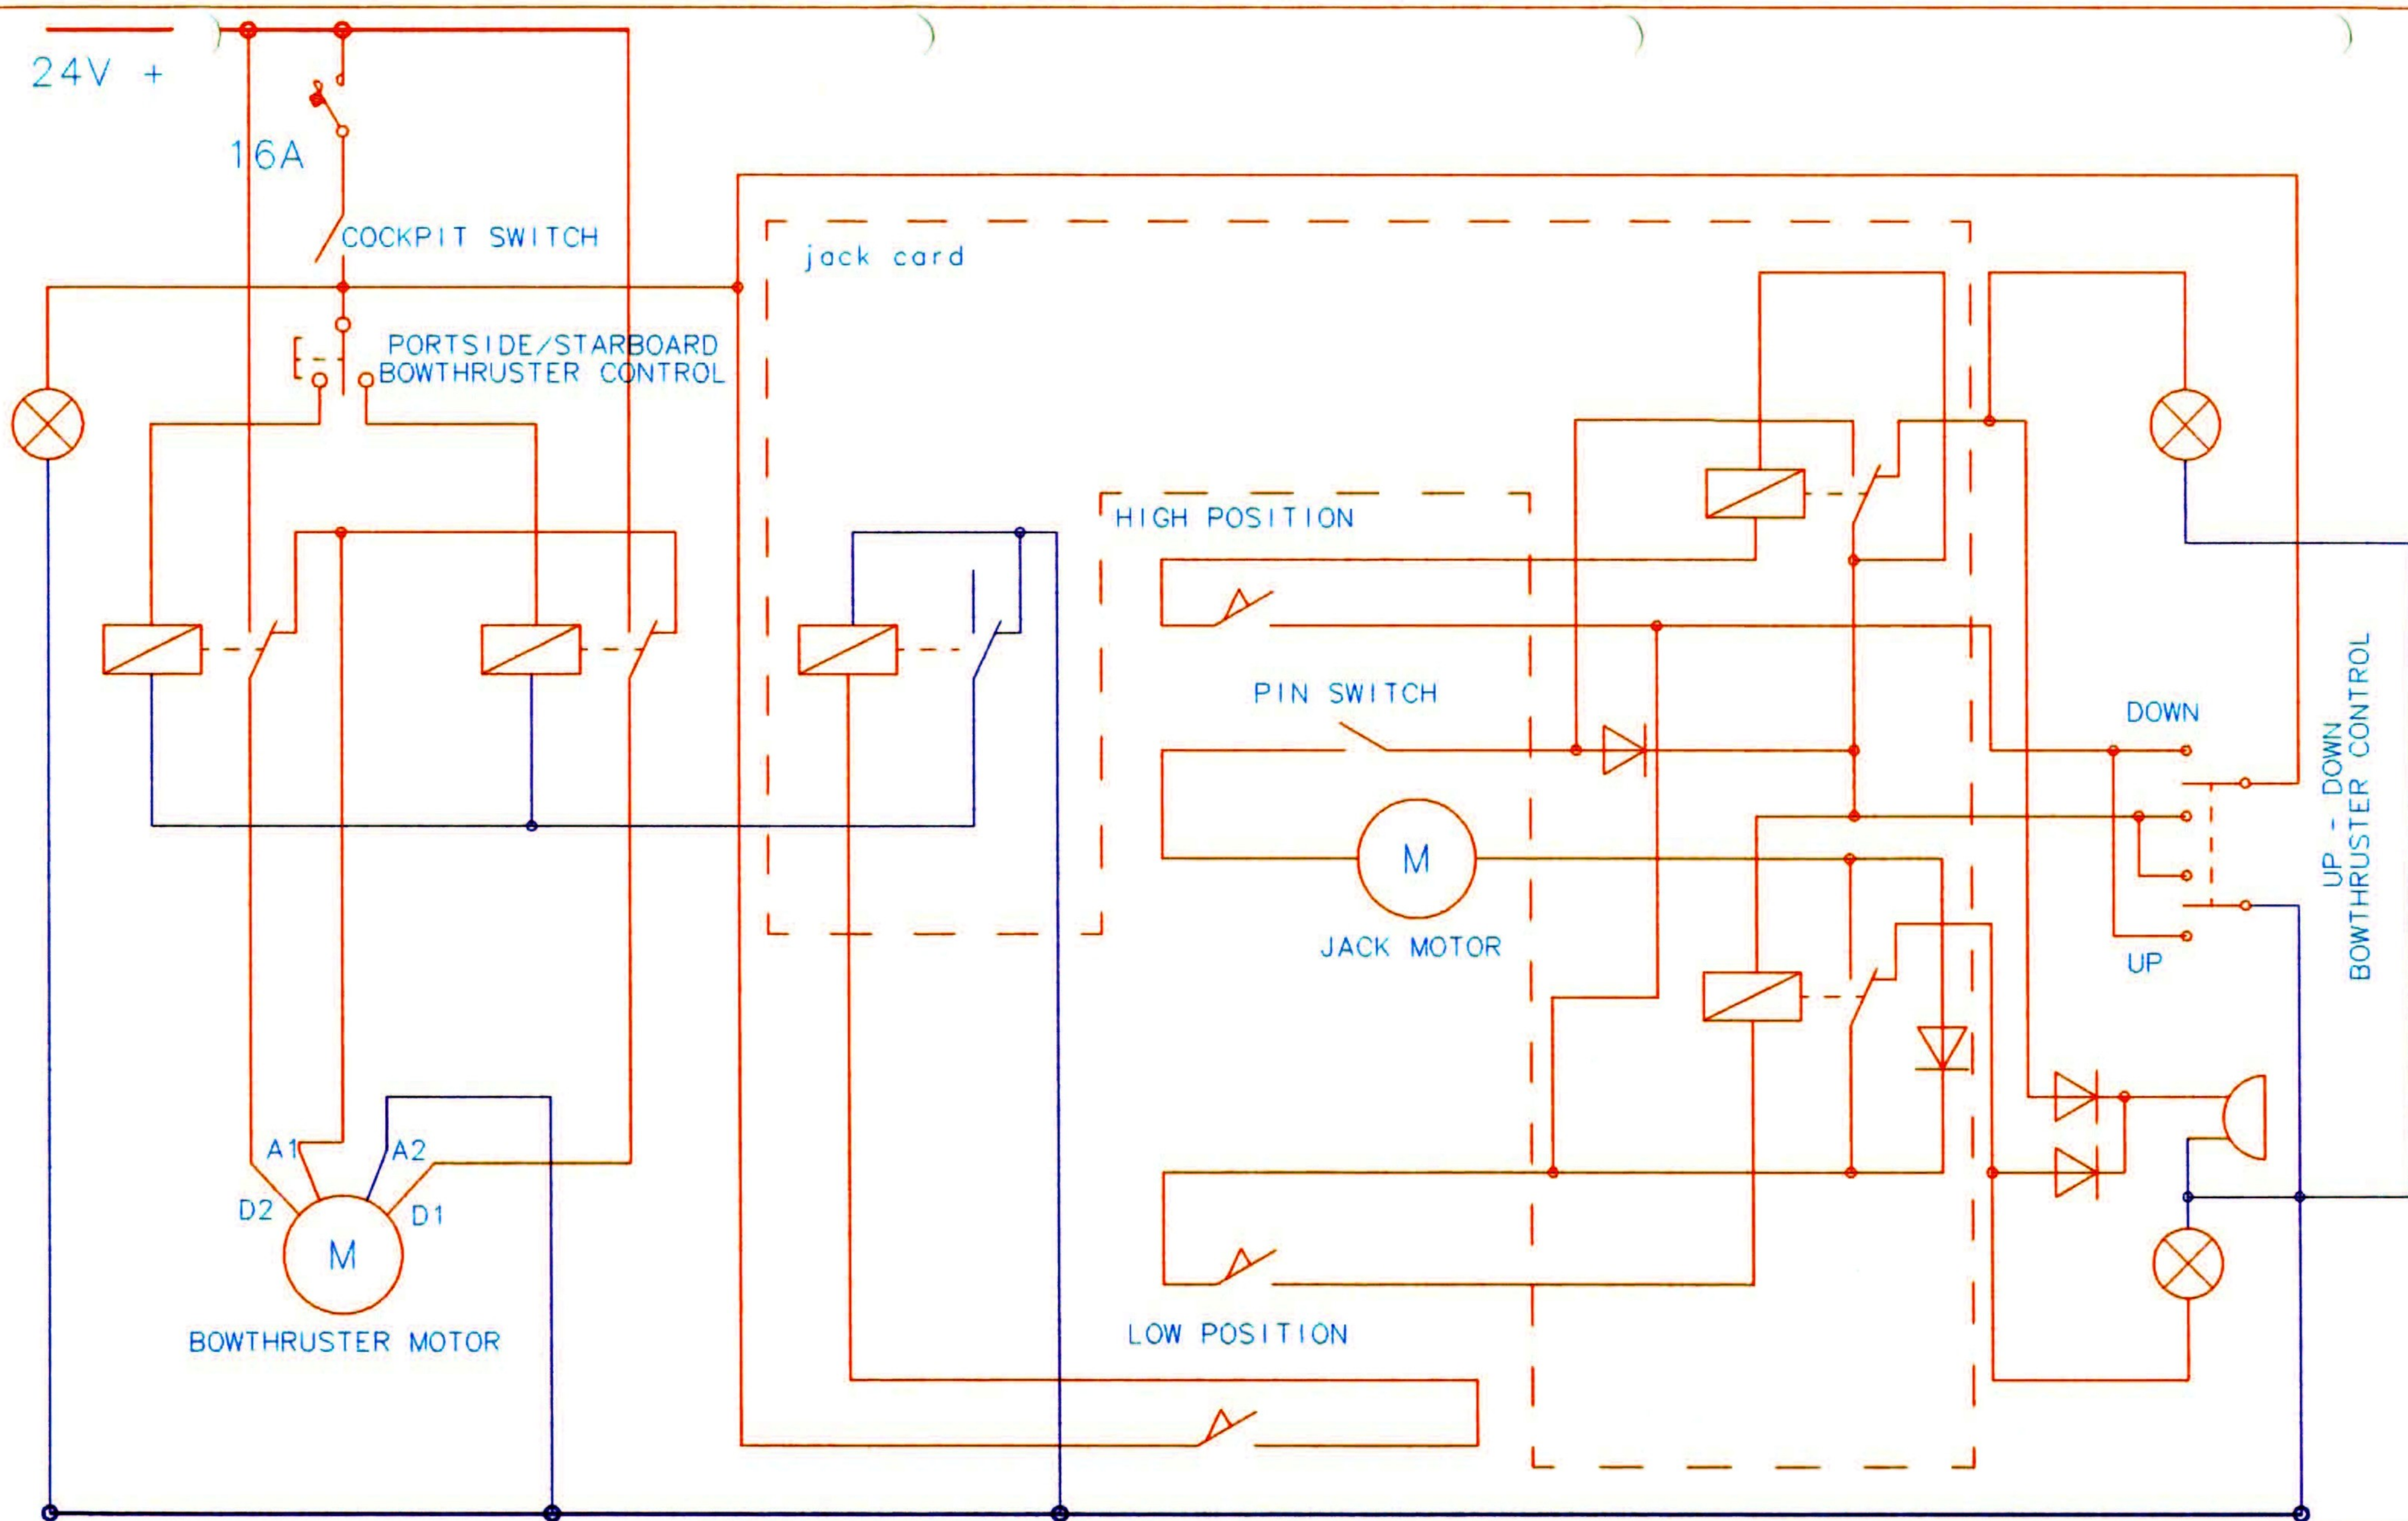

COMMAND/POWER - BOWTHRUSTER



CHANTIERS
AMEL

Ech:




Numero :

Dessine par :
L. GIBOUIN

Matiere :

Dessine le :
06/12/2001

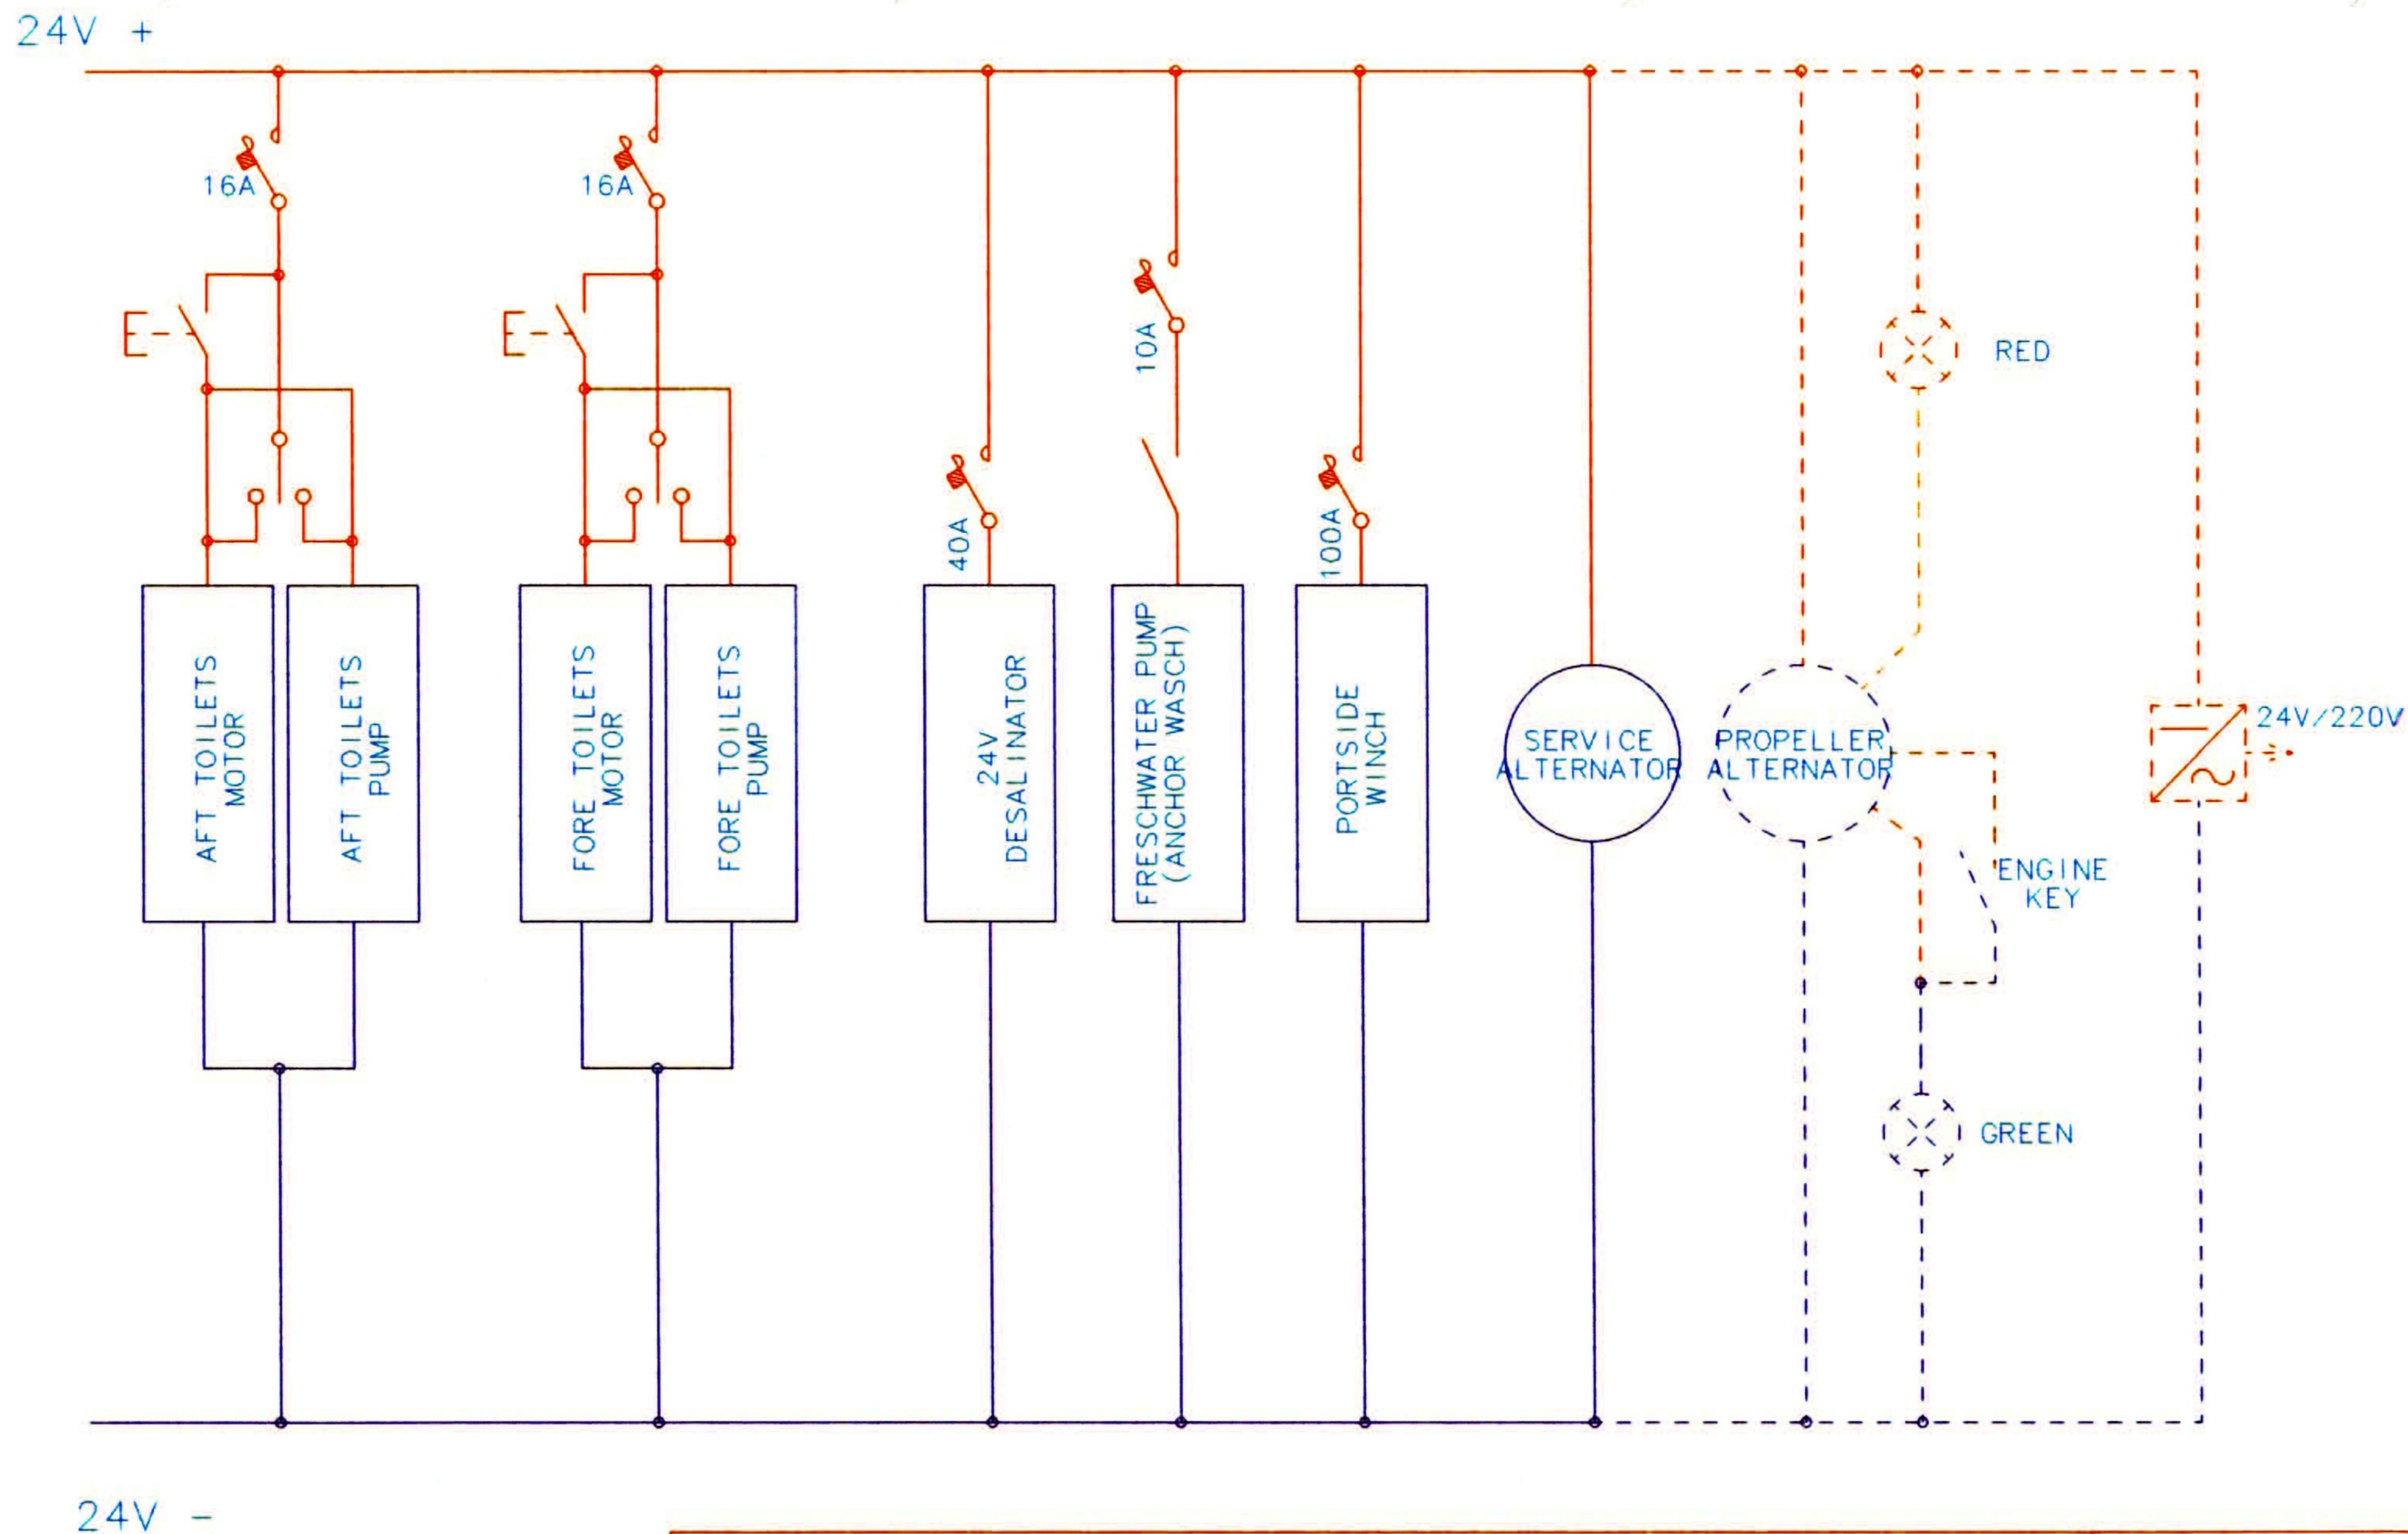

24V SERVICE
CHANTIERS
AMEL

Numero :


Matiere :

Ech:



Dessine par :
L. GIBOUIN

Dessine le :
06/12/2001

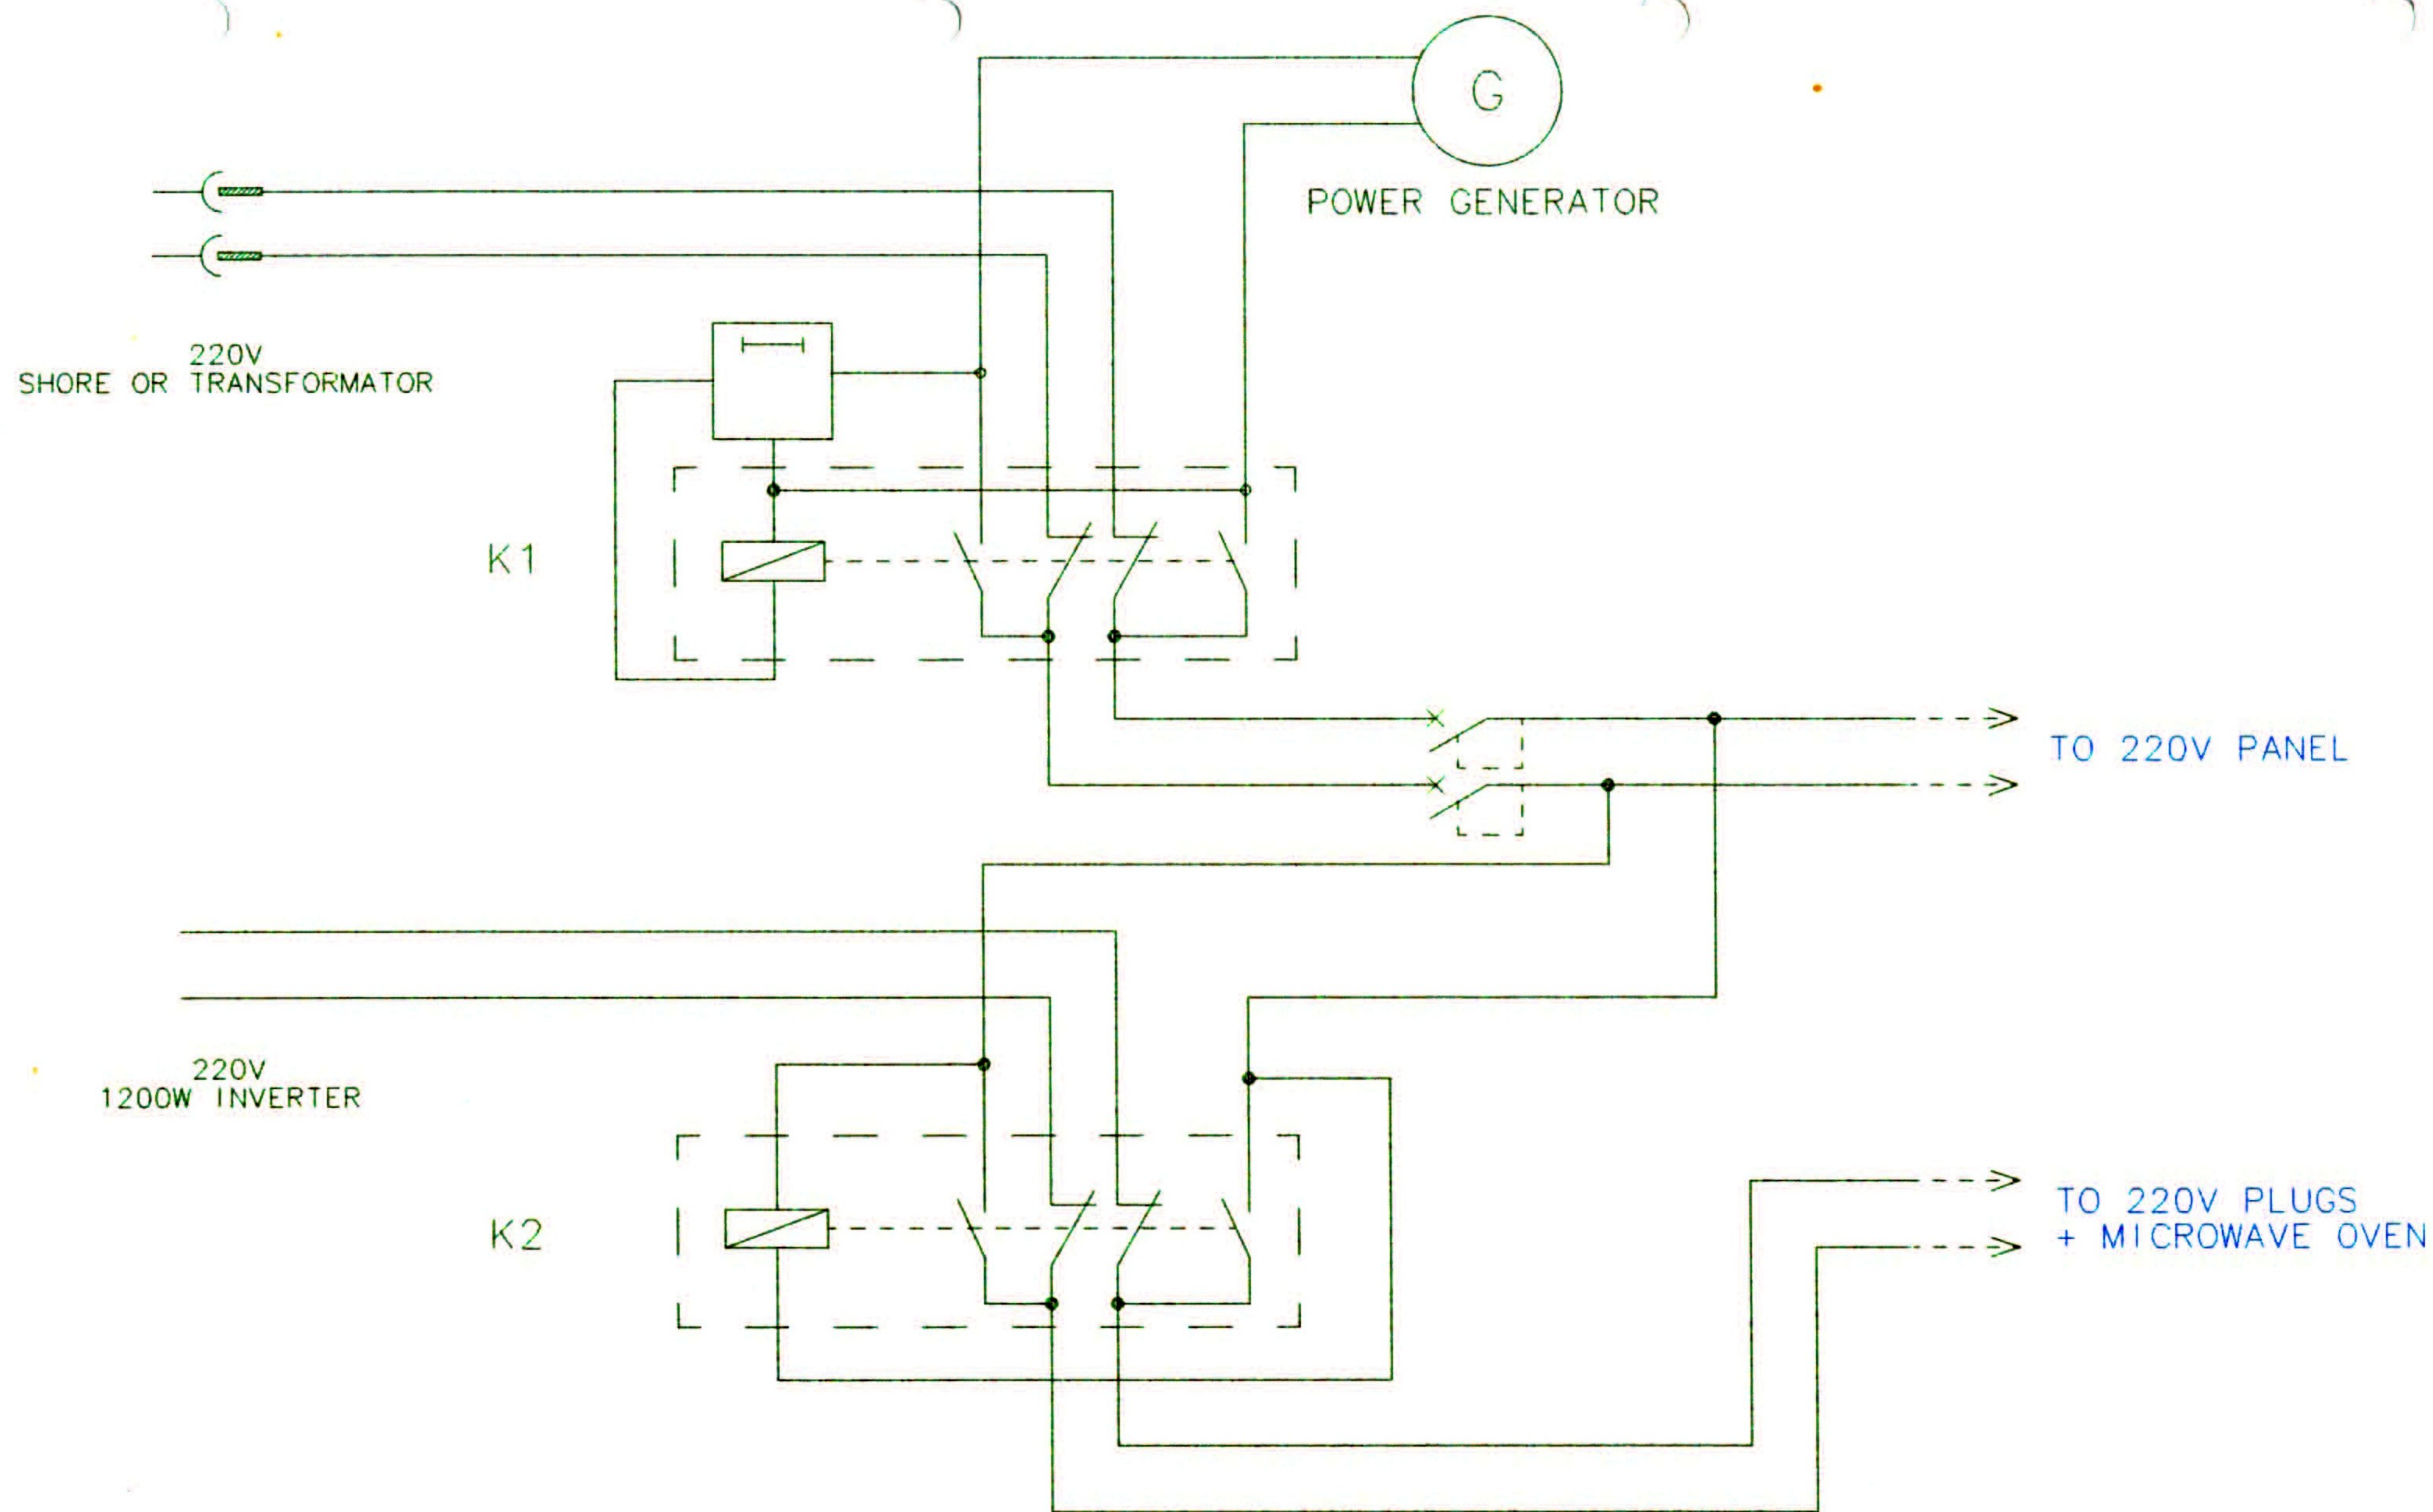

K1-K2 DETAIL



CHANTIERS
AMEL

Numero :

Matiere :

Ech:



Dessine par :
L. GIBOUIN

Dessine le :
06/12/2001